
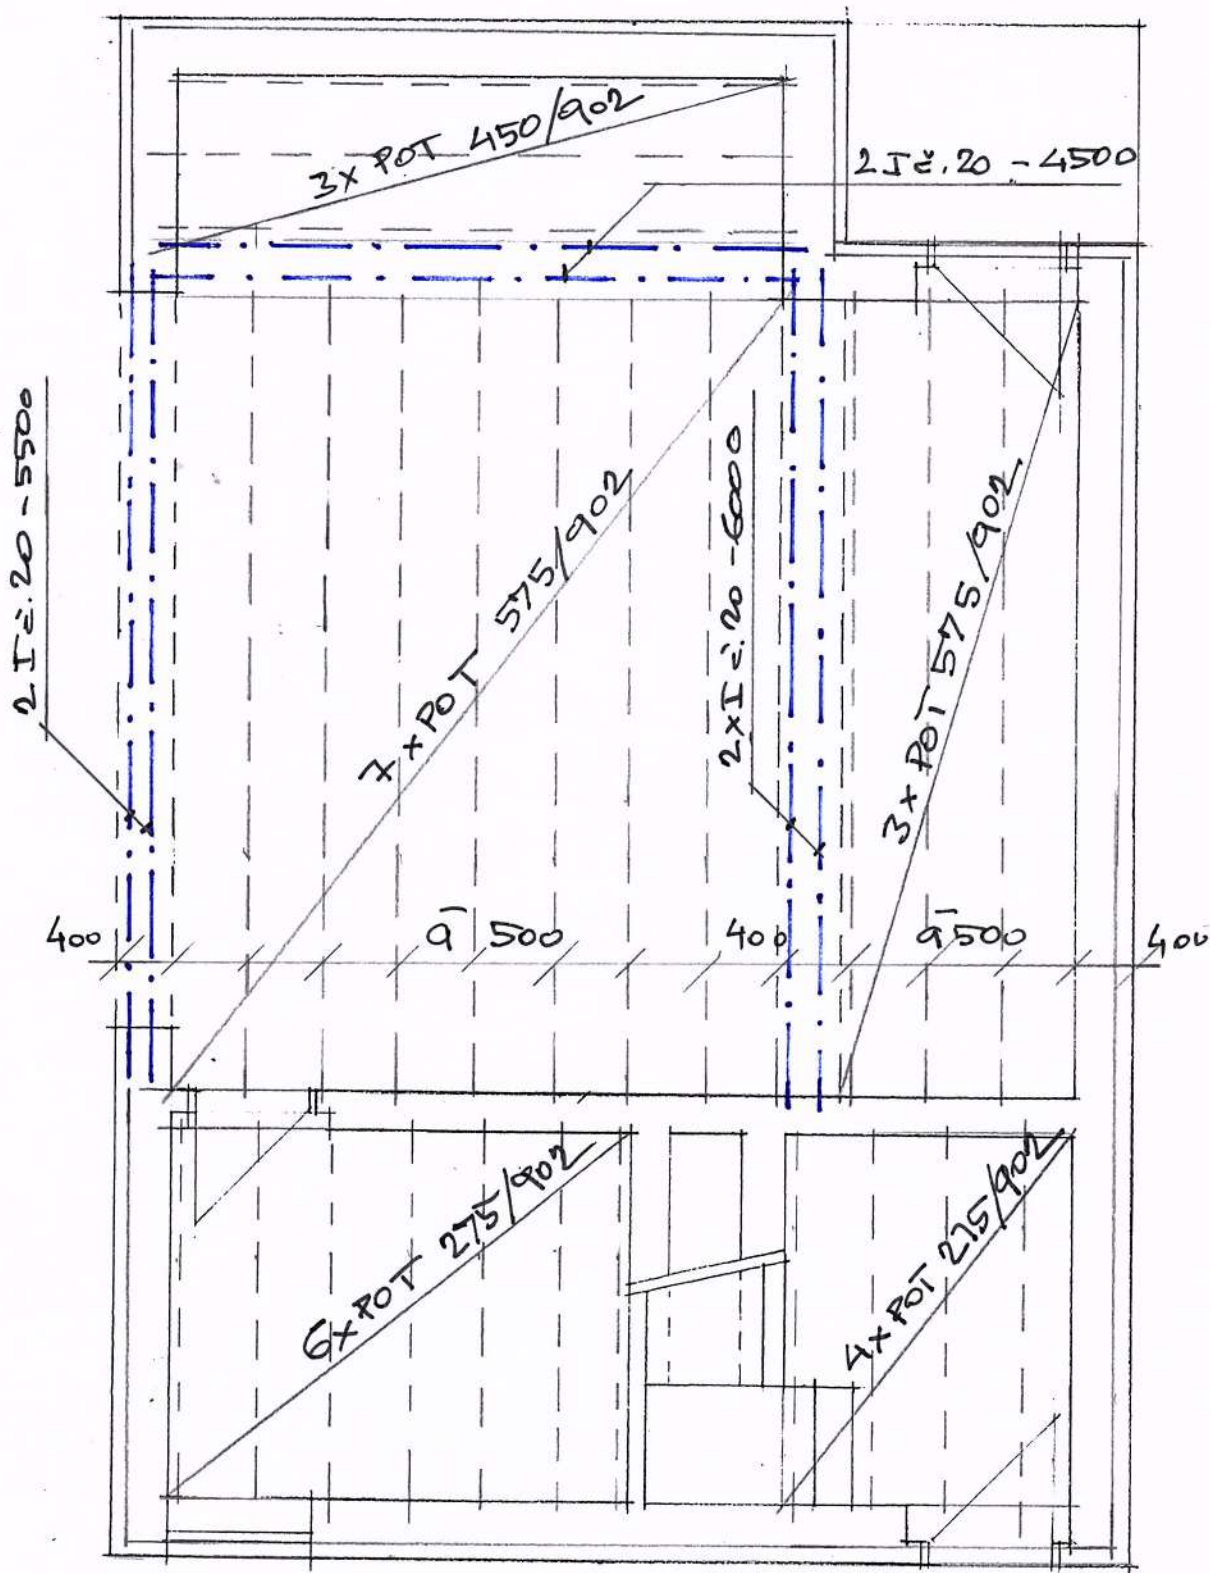


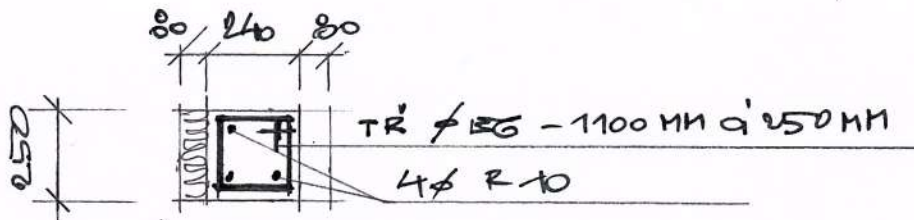

Ing.
Pavel Šíp

Digitálně podepsal
Ing. Pavel Šíp
Datum: 2026.02.23
17:18:57 +01'00'

BETON C 25/30
OCEL E 10 216
R 10 425

c3cf38b4-
c979-4ba0-
a820-
bcda8f80b12d
Digitálně podepsal
c3cf38b4-
c979-4ba0-a820-
bcda8f80b12d
Datum: 2025.12.11
17:14:21 +01'00'

akce :	Ostatní stavba - Březnická				
výkres :	Strop 1.NP				
č. výkresu :	projektant :	vypracoval :	datum :	formát :	měřítko :
d.10	Ing. Pavel Šíp	Ing. Pavel Šíp	08/25	1A4	1:50