


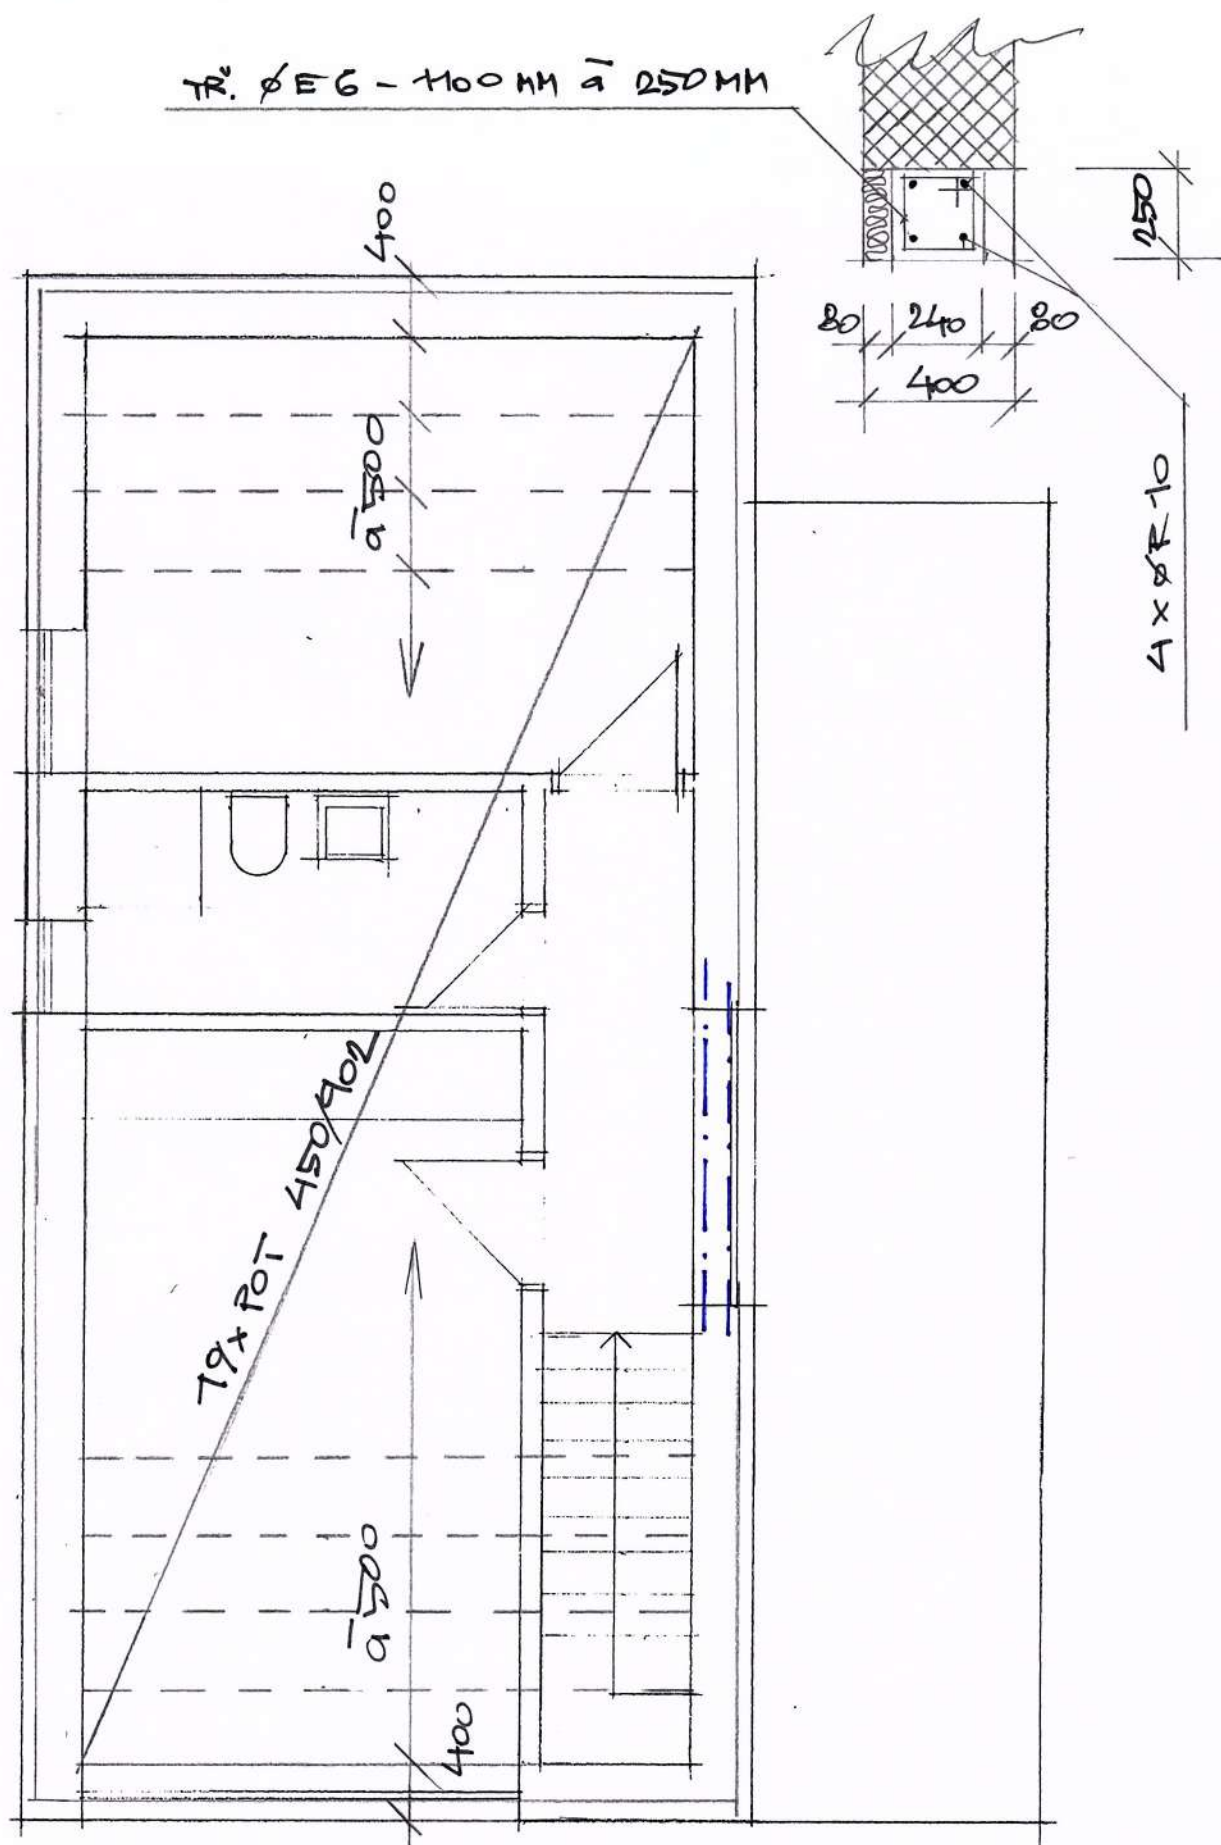

BETON C 25/30

OCEL E 10 216 R10 425

akce :	Ostatní stavba - Březnická				
výkres :	Strop 2.NP				
č. výkresu :	projektant :	vypracoval :	datum :	formát :	měřítko :
d.11	Ing. Pavel Šíp	Ing. Pavel Šíp	08/25	1A4	1:50