


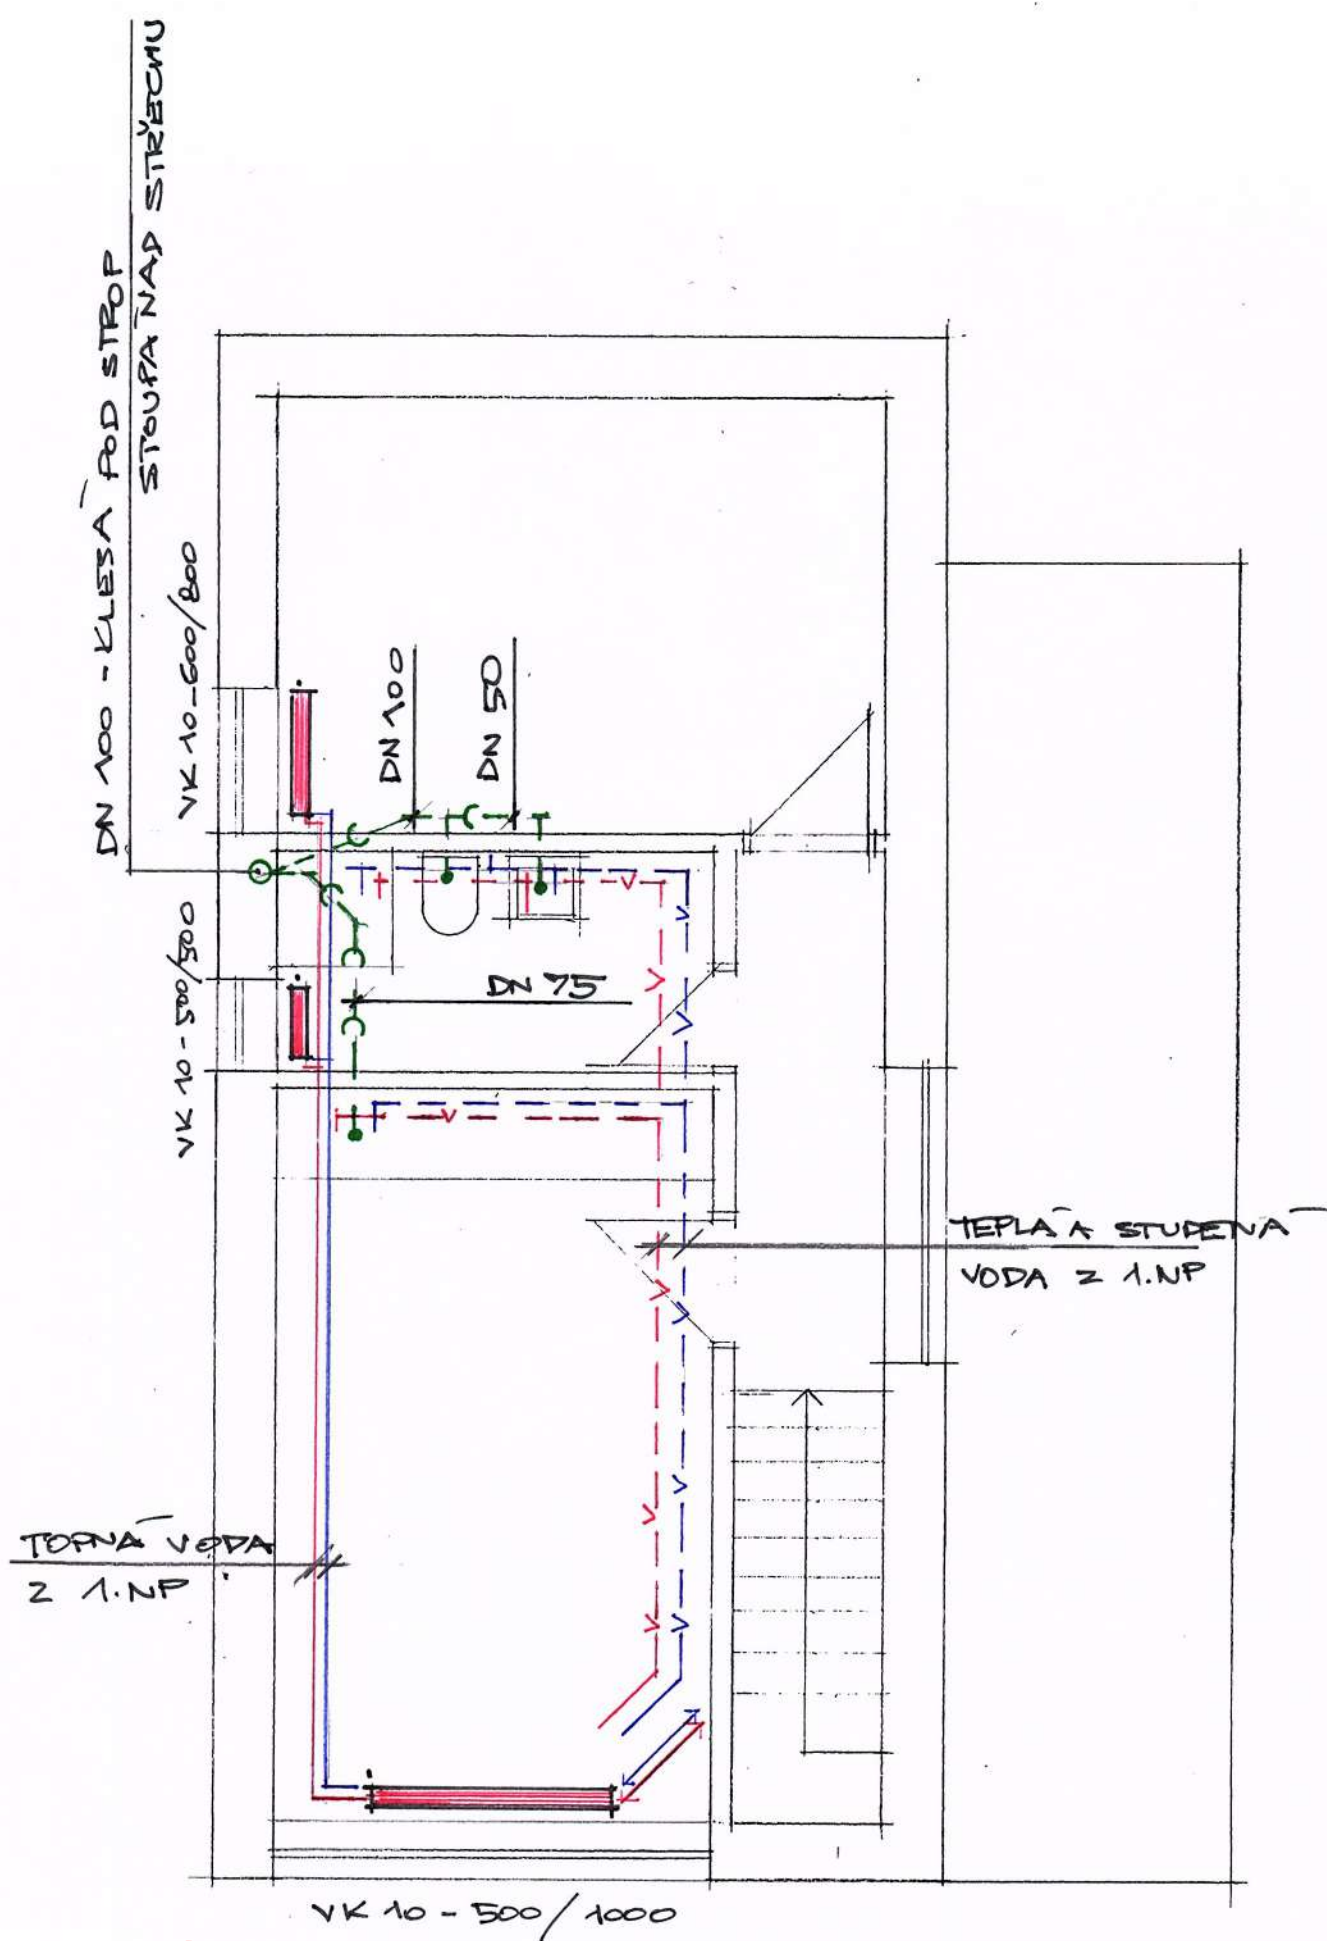

Ing.
Pavel Šíp

Digitálně podepsal
Ing. Pavel Šíp
Datum: 2026.02.23
17:22:33 +01'00'

c3cf38b4-
c979-4ba0-
a820-
bcda8f80b12d

Digitálně podepsal
c3cf38b4-c979-4ba0-
a820-bcda8f80b12d
Datum: 2025.12.11
17:17:27 +01'00'

akce :	Ostatní stavba - Březnická				
výkres :	Instalace ZTI a UT 2. NP				
č. výkresu :	projektant :	vypracoval :	datum :	formát :	měřítko :
d.13	Ing. Pavel Šíp	Ing. Pavel Šíp	08/25	1A4	1:50